

玉

Yù



3º Arquitetura e Urbanismo; Projeto de Interiores I

Professor(a): Pollyana

Acadêmicas:

Vitória

Rafaela

Ana

Sumário:


Conceito;

Moon Board;

Projeto;

Memorial;

3ºArquitetura e Urbanismo; Projeto de Interiores I
Professor(a): Pollyana
Acadêmicas:
Vitória
Rafaela
Ana

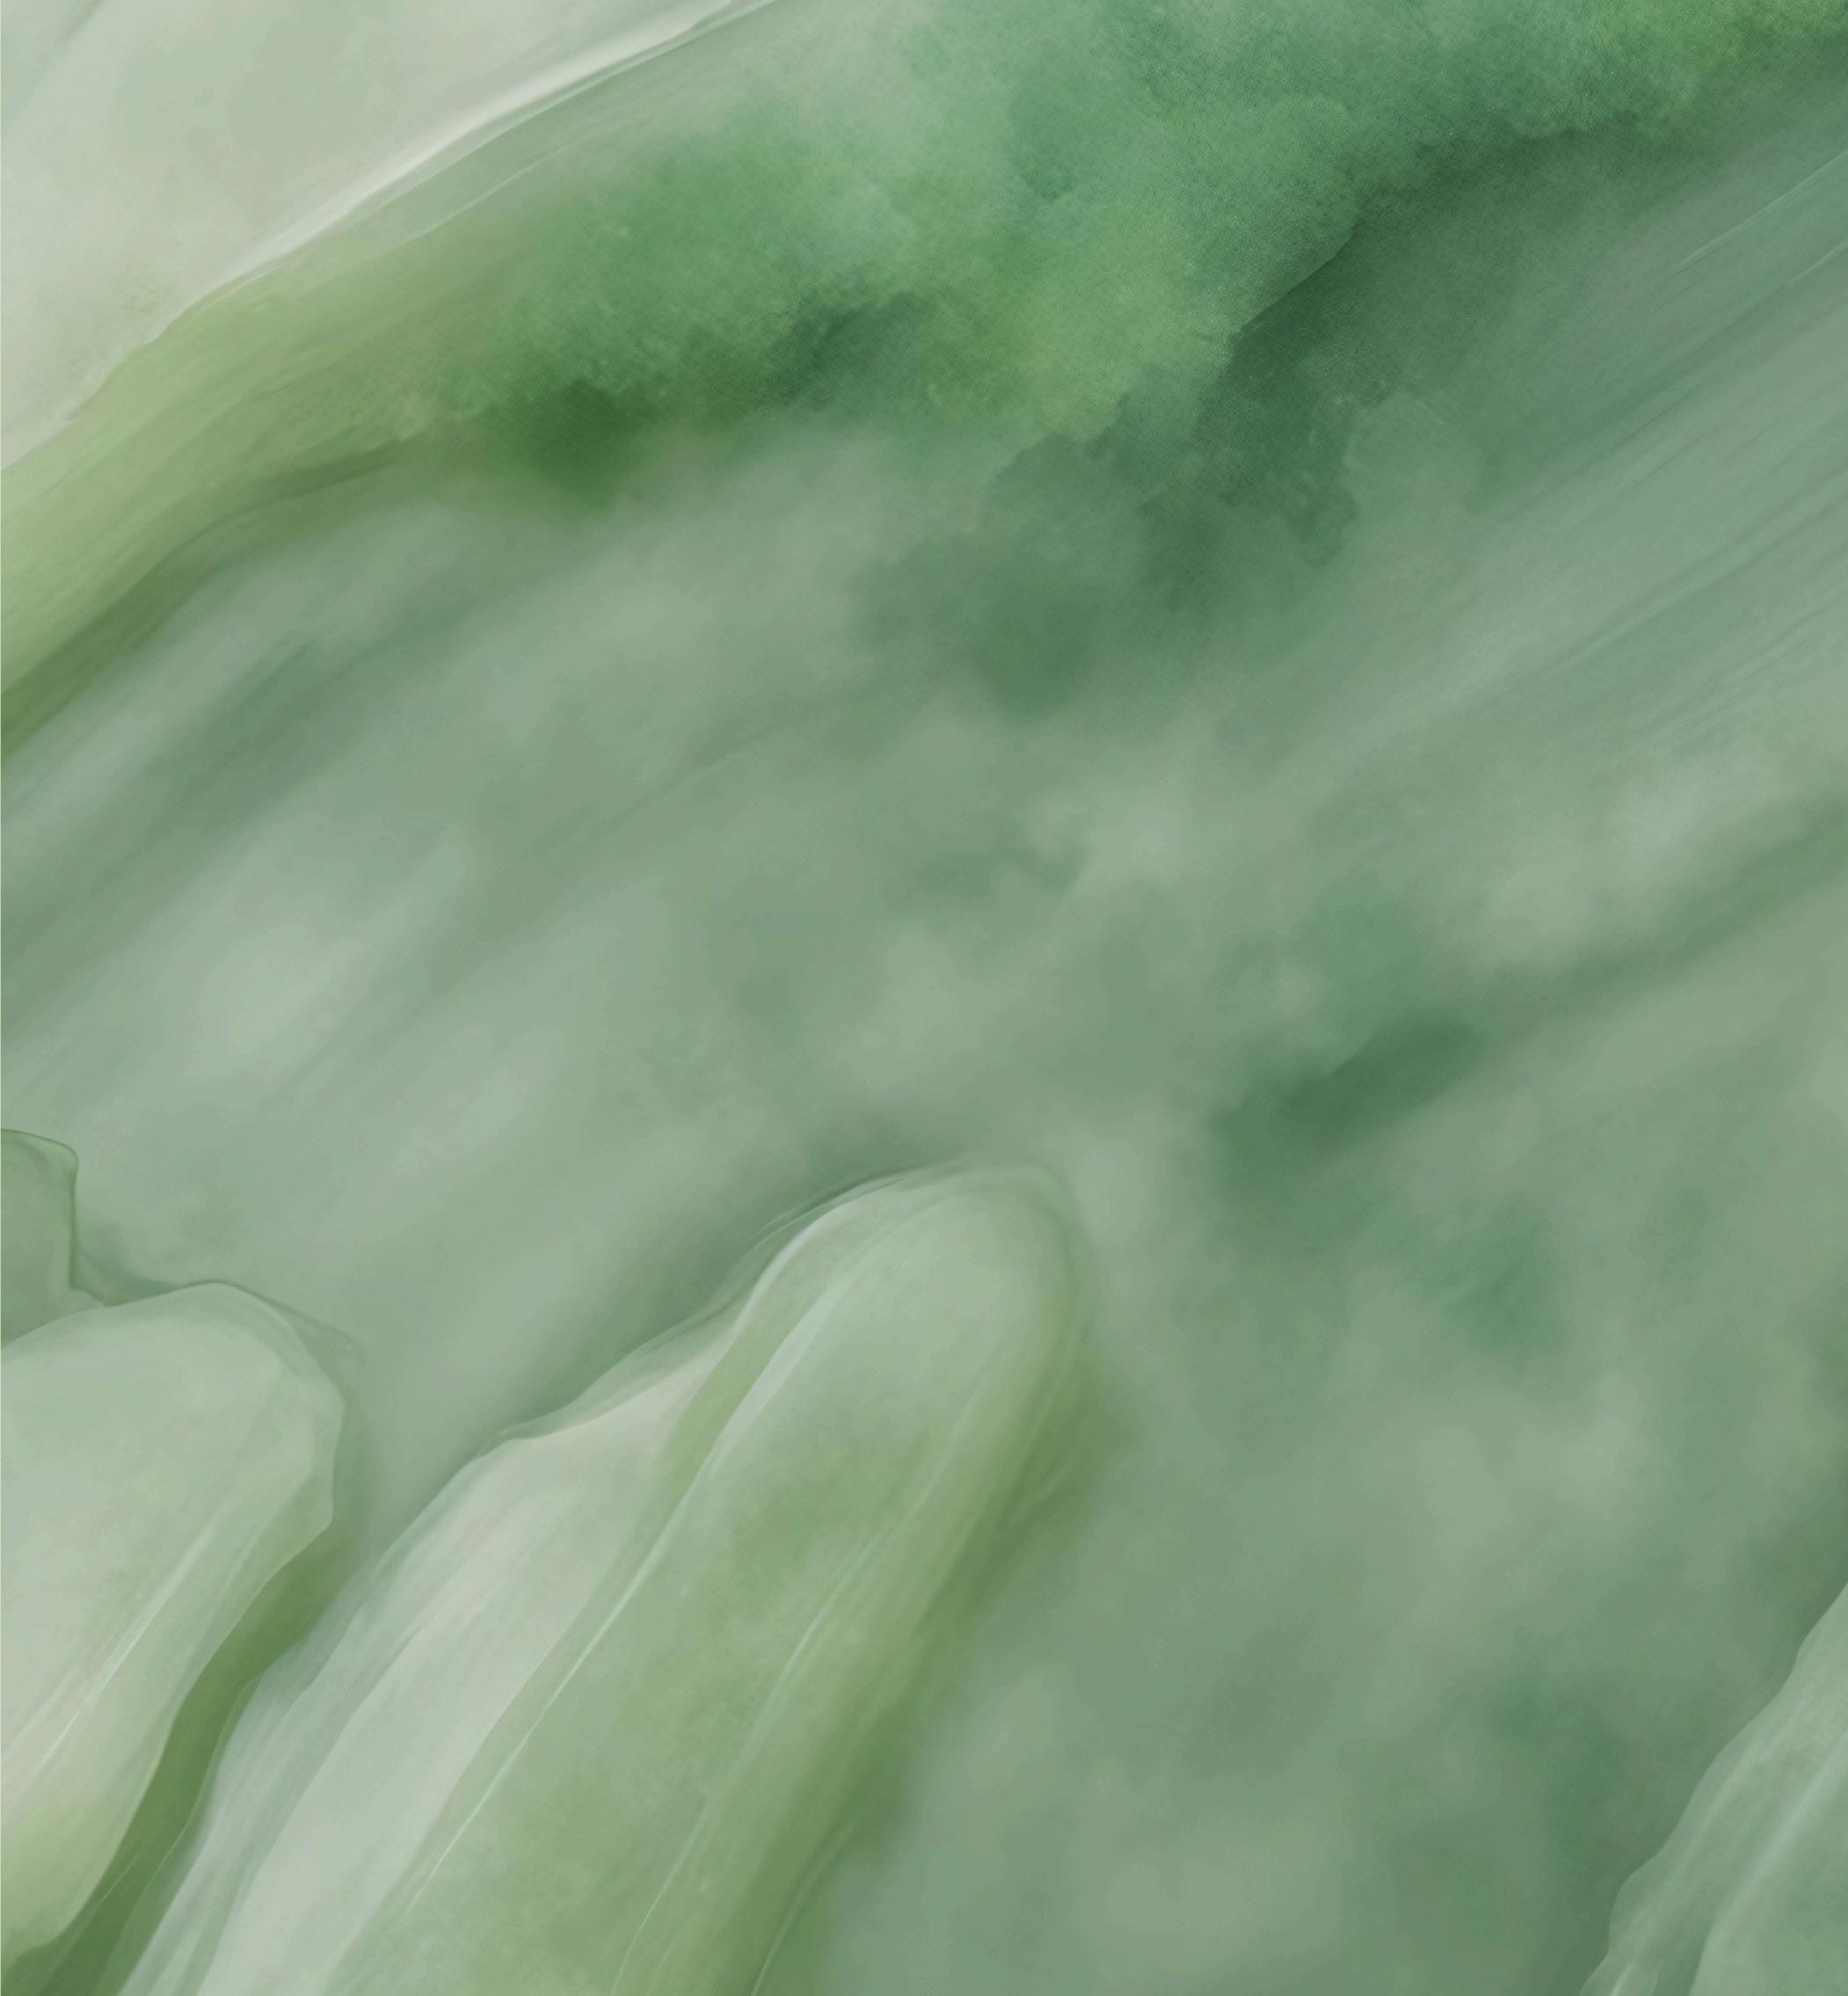

Conceito

JADE

Pedra conhecida naturalmente pela sua beleza, especialmente na cultura chinesa a sua importância vai além dos aspectos estéticos e passa a ser mais profundo. Entre muitas das interpretações da Jade, podemos citar as principais sendo associada a realeza. Mas foi por conta do filosofo Confúcio que fez a Jade ser lida como uma metáfora para virtude, bondade, sabedoria, justiça, civilidade, música, sinceridade, verdade, Céu e Terra. Ainda acredita-se que tem o poder de afastar o mal e a má sorte, além de promover a saúde e a boa sorte.

Apesar de ser carregada de interpretações das mais diversas, no Projeto **Yù** a Jade aqui tem o papel principal de resgatar a espiritualidade, pureza e saúde. Na cultura chinesa, diz que o ouro pode ter um preço, mas o jade não tem preço, tal qual essas qualidades anteriormente faladas, que não devem de forma nenhuma serem negligenciadas. Trazendo para interiores, o objetivo é proporcionar através das cores, elementos, iluminação, móveis e elementos decorativos uma lembrança amigável da joia e suas propriedades positivas como a virtude, bem-estar,



3º Arquitetura e Urbanismo; Projeto de Interiores I

Professor(a): Pollyana


Acadêmicas:

Vitória

Rafaela

Ana

MOON BOARD

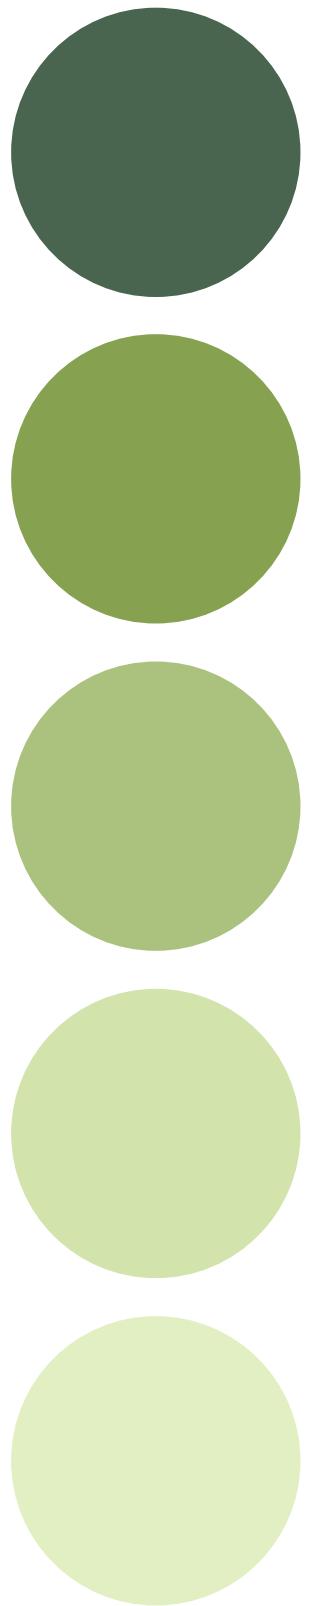



ALUNOS: **RAFAELA
ANA
VITORIA**

DISCIPLINA: **PROJETO DE INTERIORES I**

R.A.:

TURMA.:ARQUITETURA E URBANISMO VISTO:

FOLHA Nº:

3 SEMESTRE


05

PROFESSORA: **POLLYANA**


DATA: **23/04/2025**

20

PLANTA BAIXA

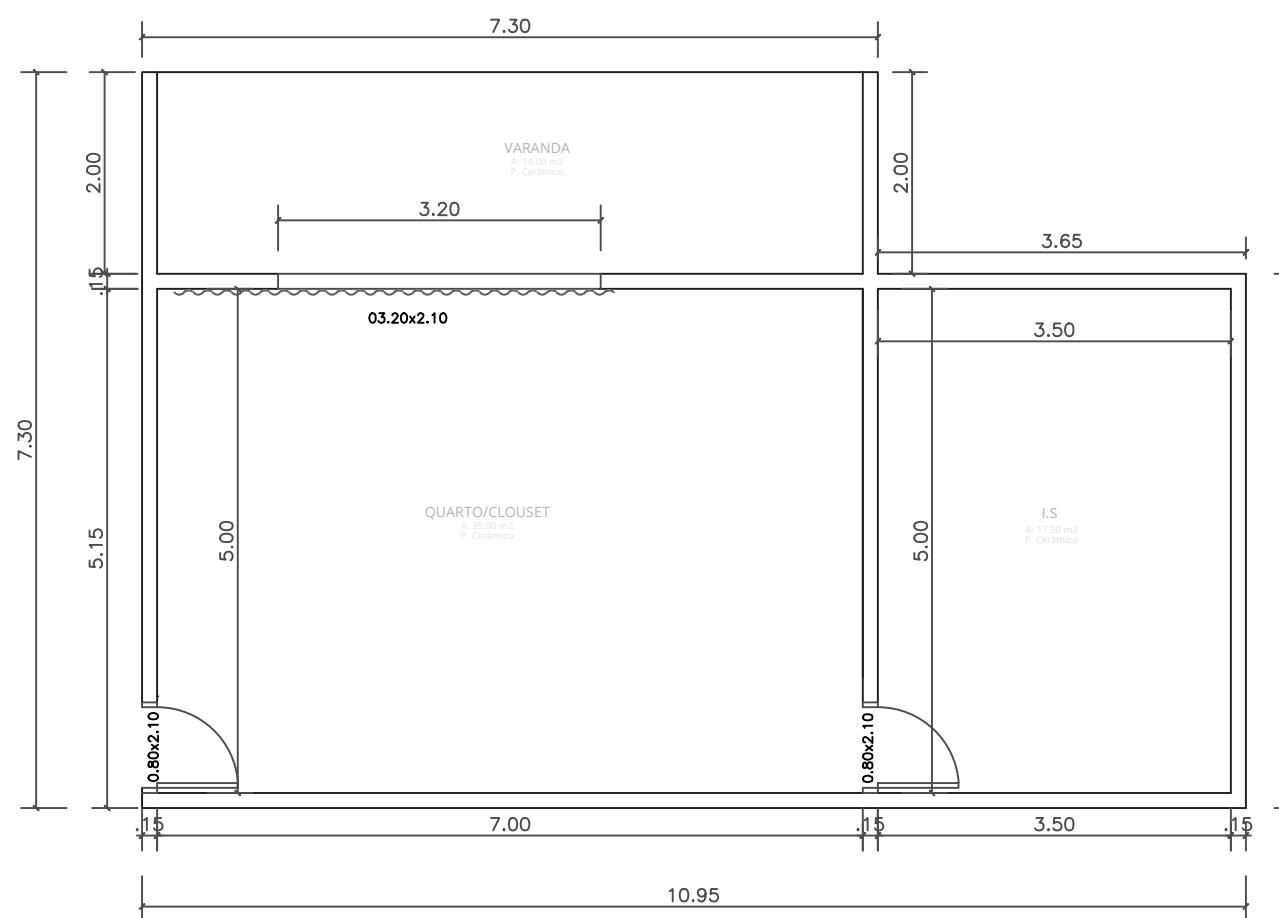

01 PLANTA BAIXA
ESC.: 1/75

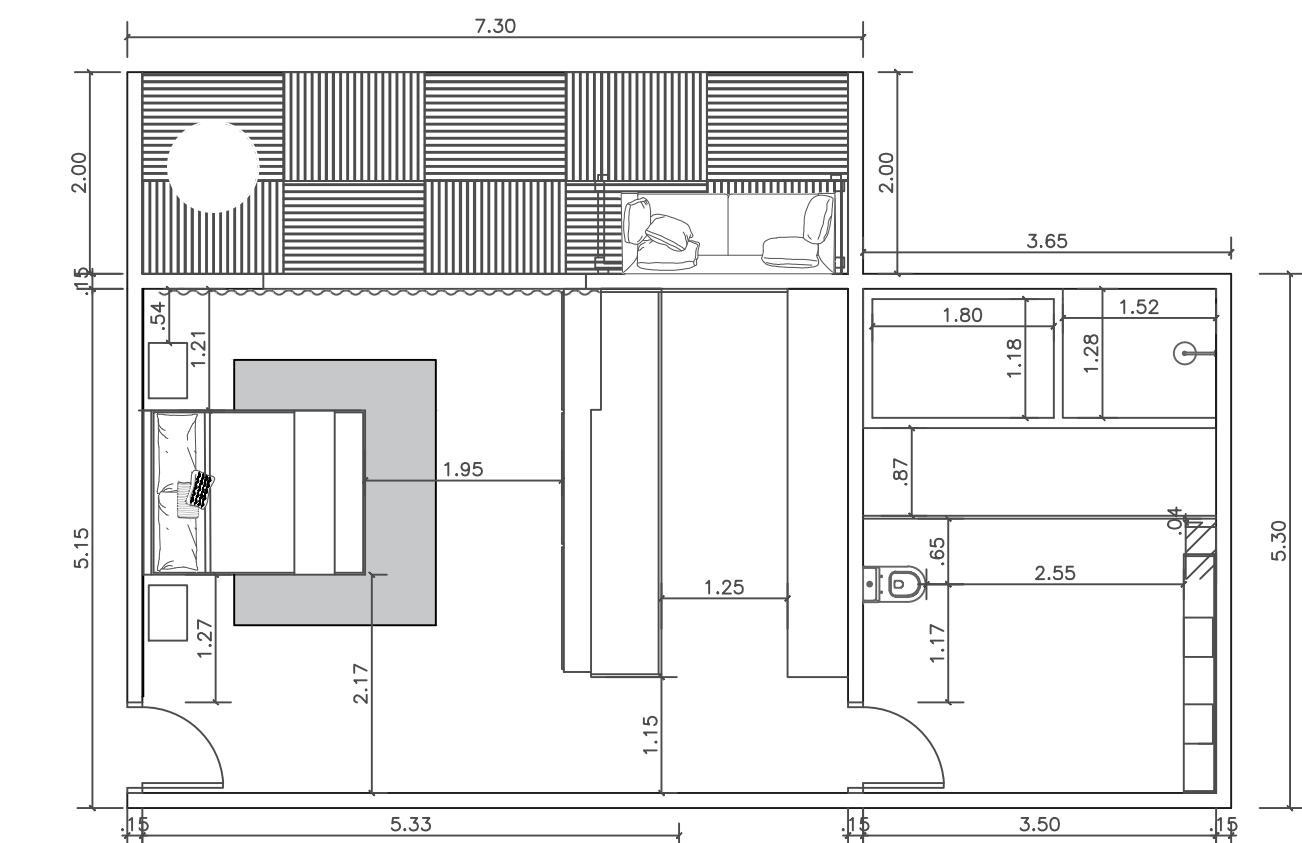

02 PLANTA COM LAYOUT
ESC.: 1/75

ALUNOS: RAFAELA BEATRIZ RIBEIRO RODRIGUES
ANA LAURA OLIVEIRA TAQUES
VITORIA LORANA DA SILVA DOS SANTOS

DISCIPLINA: PROJETO DE INTERIORES I

R.A.: 177377-2024
187322-2024
168630-2024

PROFESSORA: POLLYANA ROMAGNOLI TAMANINI

TURMA: ARQUITETURA E URBANISMO
3 SEMESTRE

VISTO:



FOLHA N°:

06

DATA: 23/04/2025



20

PLANTA DE FORRO

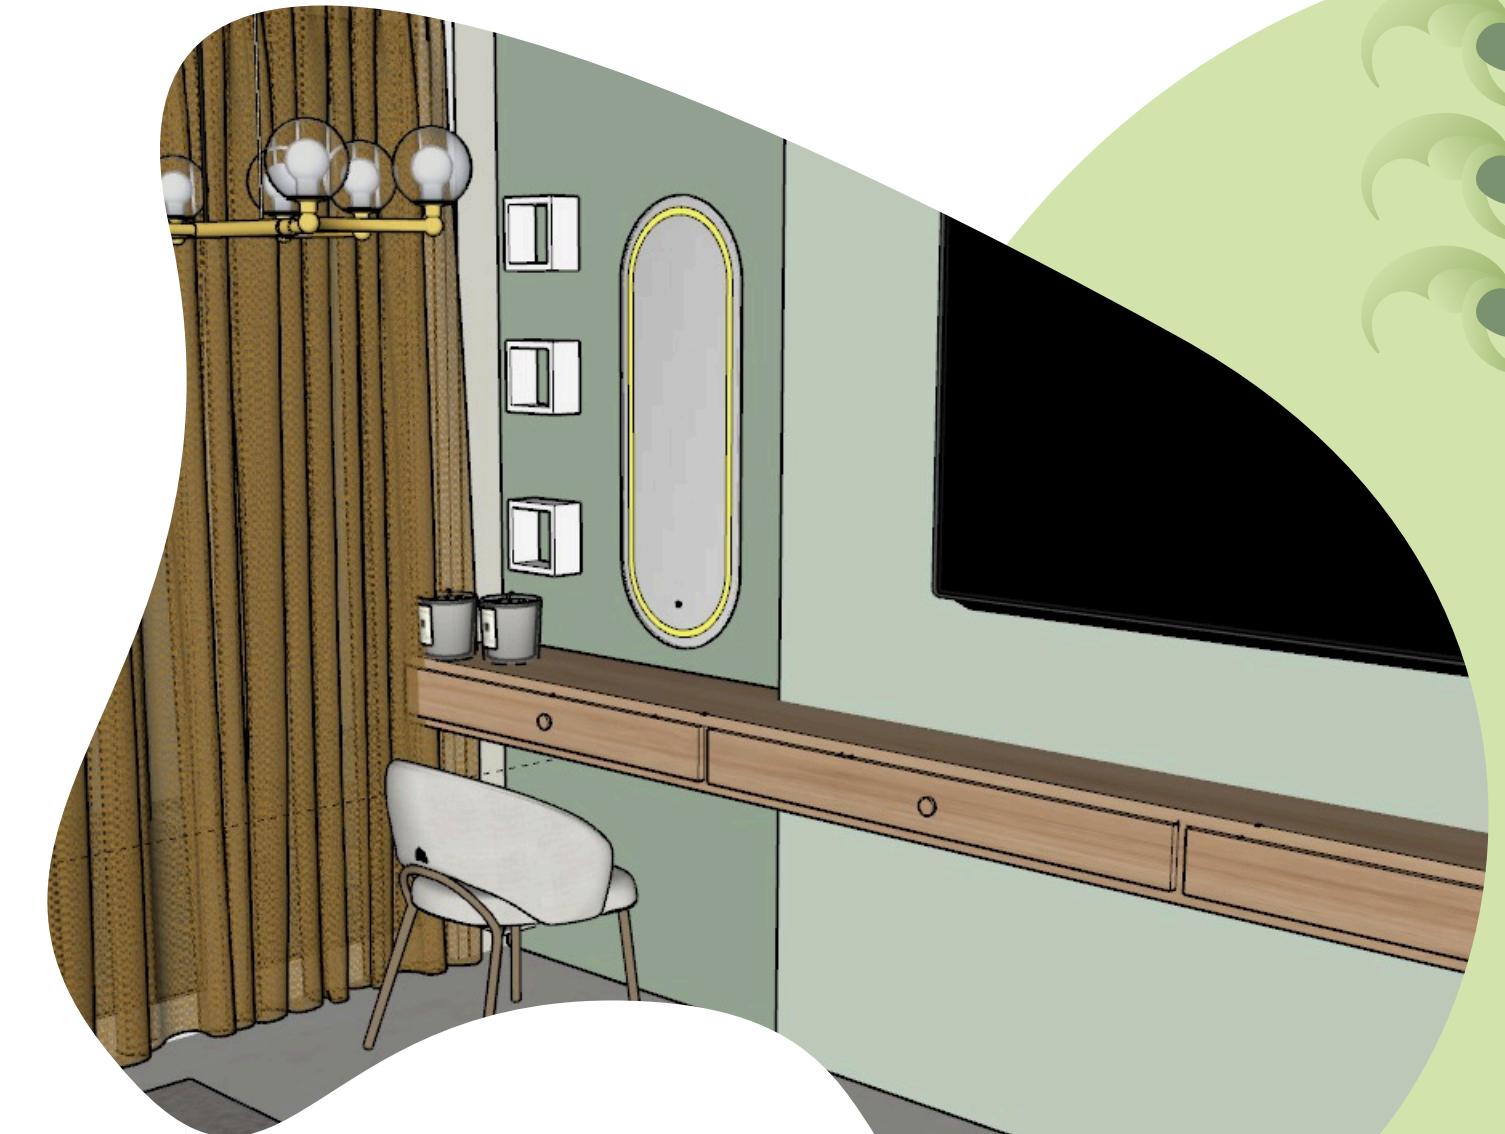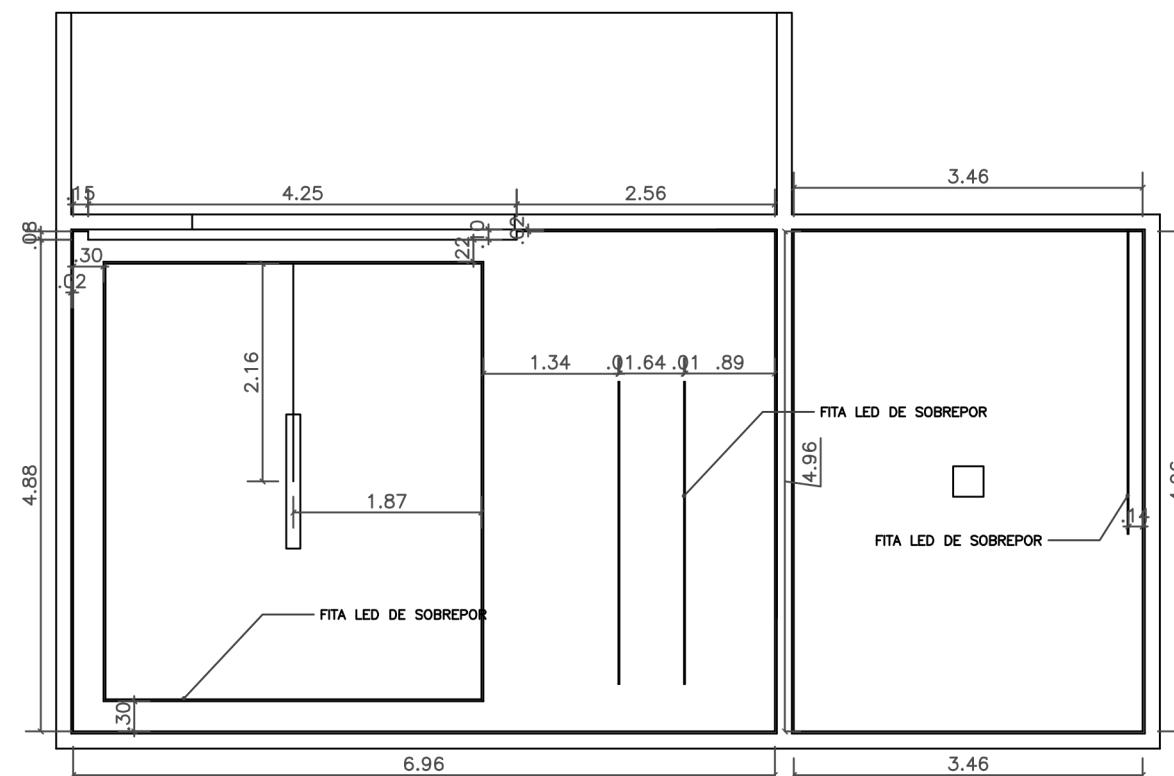

ALUNOS: RAFAELA ANA VITORIA	R.A.:	TURMA: ARQUITETURA E URBANISMO 3 SEMESTRE	VISTO:	FOLHA N°: 07
DISCIPLINA: PROJETO DE INTERIORES I	PROFESSORA: POLLYANA		DATA: 23/04/2025	20

VISTA DO BANHEIRO

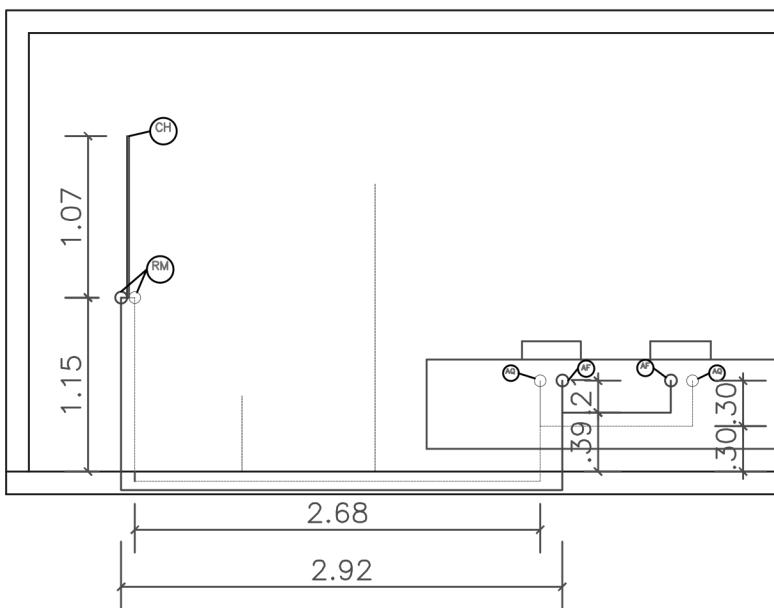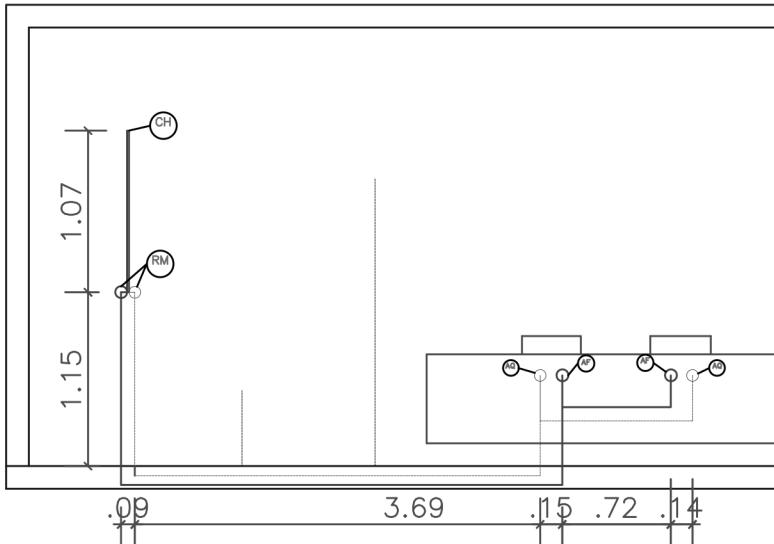

vista frontal

ESC.: 1/50

ALUNOS: RAFAELA
ANA
VITORIA

DISCIPLINA: PROJETO DE INTERIORES I



04

R.A.:
PROFESSORA:
POLLYANA

TURMA: ARQUITETURA E URBANISMO
3 SEMESTRE

VISTO:


FOLHA N°:

08

DATA: 23/04/2025


20

VISTA DO BANHEIRO

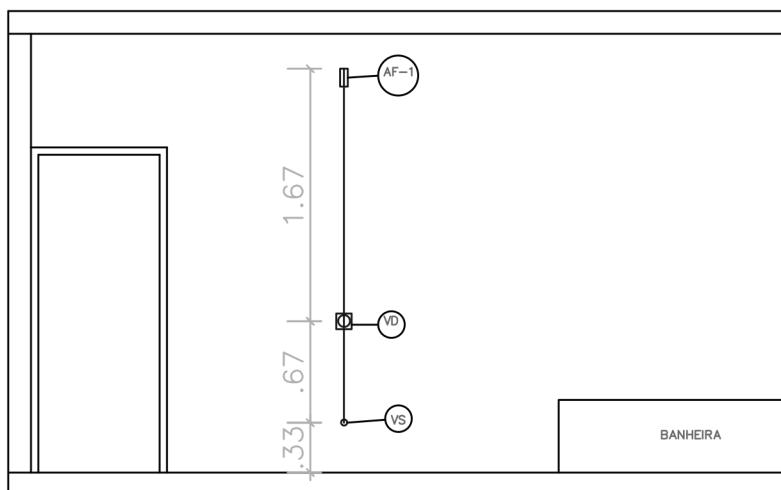

LEGENDA DE IDENTIFICAÇÃO	
●	PONTO DE ESGOTO
CH	CHUVEIRO DUCHA
VD □	VALVULA DE DESGARGA
VS	VASO SANITÁRIO COM VALVULA DE DESCARGA
LV	LAVATORIO
RM	REGISTRO MONOCOMANDO

LEGENDA DE CONDUTOS	
ÁGUA FRIA	
ÁGUA QUENTE	

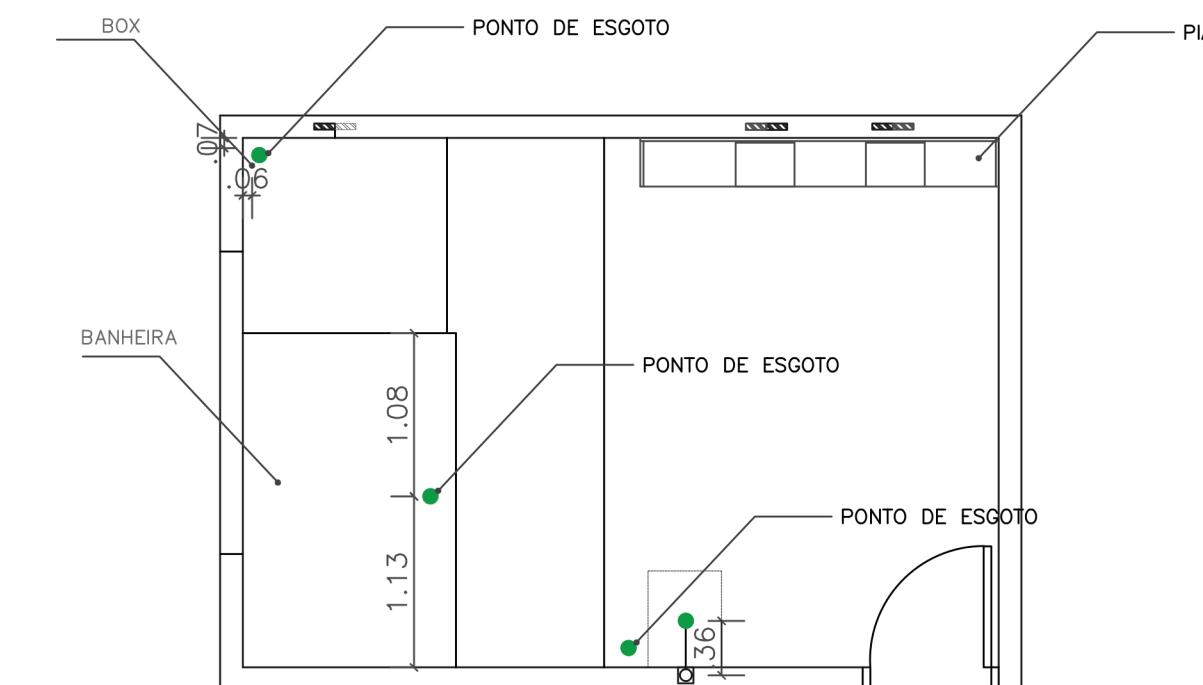

ALUNOS: RAFAELA
ANA
VITORIA

DISCIPLINA: PROJETO DE INTERIORES I

R.A.:

TURMA: ARQUITETURA E URBANISMO
3 SEMESTRE

VISTO:

FOLHA N°:


09

PROFESSORA: POLLYANA

DATA: 23/04/2025


20

DETALHAMENTO

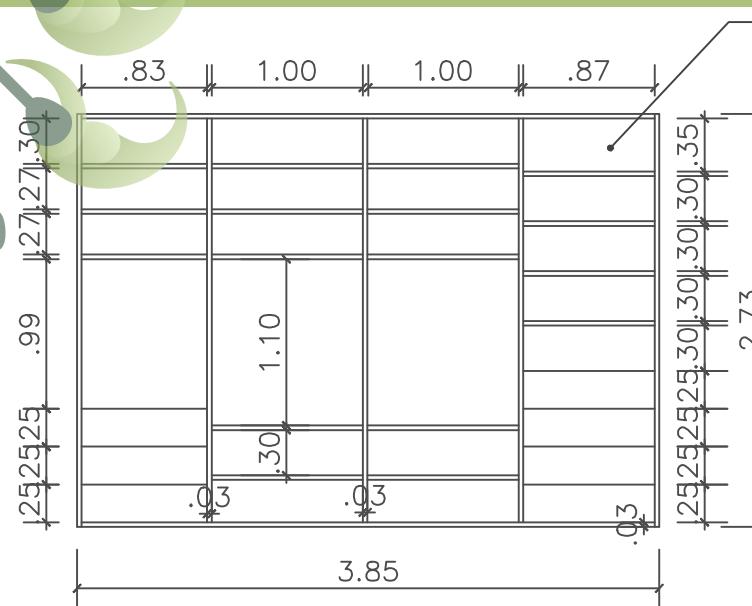


VISTA 1: VISTA FRONTAL

ESC.: 1/50

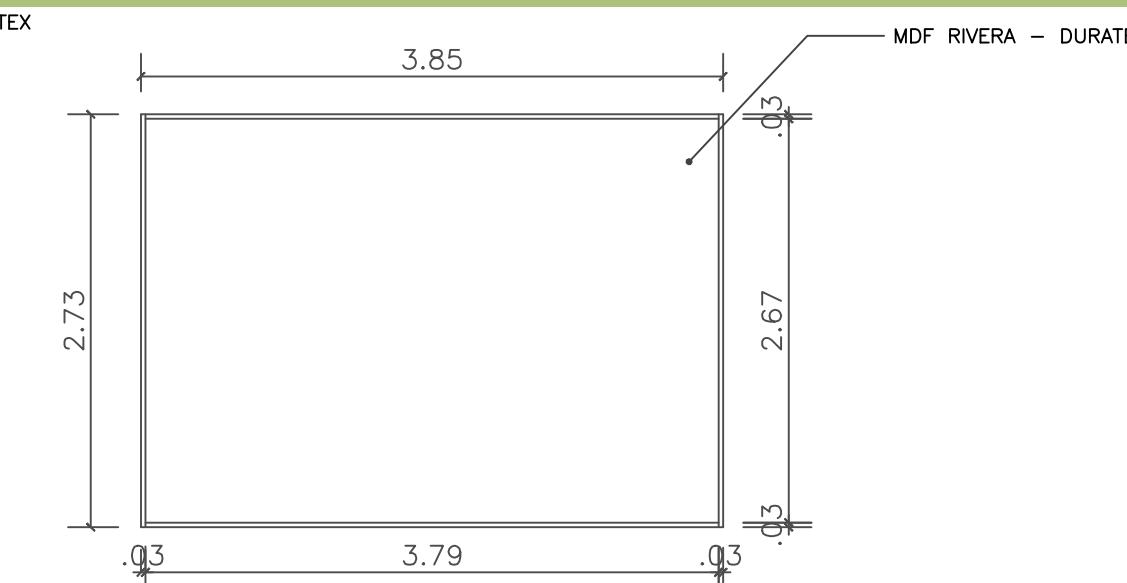


VISTA 2 : VISTA TRASEIRA

ESC.: 1/50

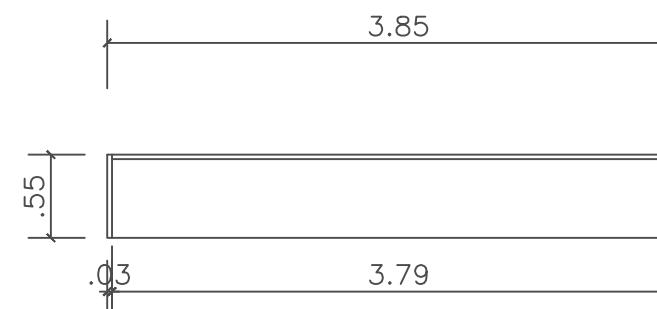


VISTA 3: VISTA SUPERIOR

ESC.: 1/50

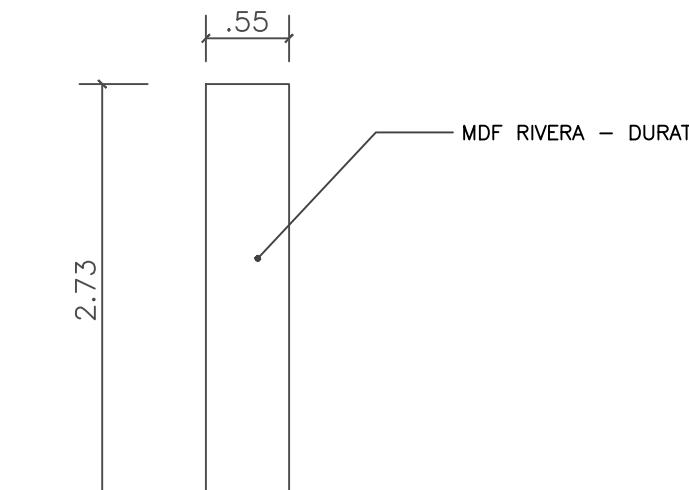

VISTA 4: VISTA LATERAL ESQUERDA

ESC.: 1/50

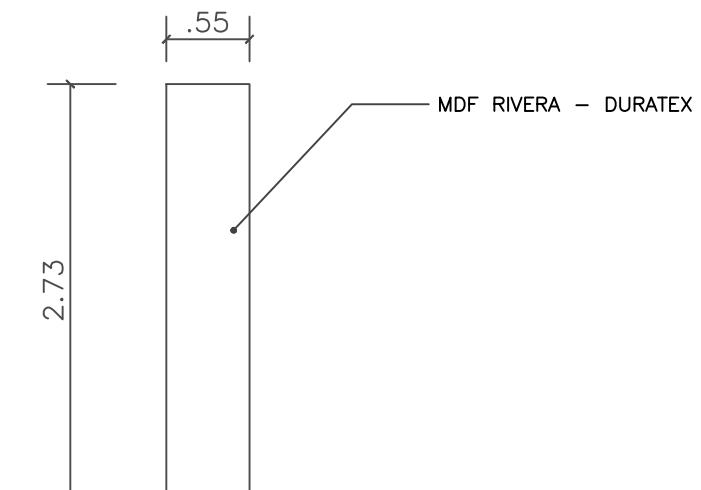

VISTA 5: VISTA LATERAL DIREITA

ESC.: 1/50

07

DETALHAMENTO DE MOBILIARIO - CLOSET 1

ESC.: 1/75

ALUNOS: RAFAELA BEATRIZ RIBEIRO RODRIGUES
ANA LAURA OLIVEIRA TAQUES
VITORIA LORANA DA SILVA DOS SANTOS

DISCIPLINA: PROJETO DE INTERIORES I

R.A.: 177377-2024
187322-2024
168630-2024

PROFESSORA: POLLYANA ROMAGNOLI TAMANINI

TURMA: ARQUITETURA E URBANISMO
3 SEMESTRE

VISTO:

FOLHA N°:

10

20

DATA: 23/04/2025

DETALHAMENTO

This technical drawing illustrates a door assembly with various layers and dimensions. The top horizontal bar is labeled "MDF BP VERDE JADE". The left vertical bar is labeled "MDF CRISTAL - DURATEX". The right vertical bar is labeled "MDF RIVERA - DURATEX". A central vertical bar has a thickness of .10. The total height of the left side is 3.80, and the total height of the right side is 3.85. The middle section has a height of 3.79. The bottom horizontal bar has a width of .97, with a .70 gap between two internal vertical lines. The overall width of the bottom section is .27. The bottom-most layer is labeled "F RIVERA - DURATEX".

VISTA 1 - VISTA FRONTAL

VISTA 1: VISTA FRONTE

ESC.: 1

The technical drawing illustrates the construction of a cabinet door. It features a central panel with a thickness of .20 inches, flanked by vertical stiles of .03 inches. The top and bottom edges are composed of MDF BP VERDE JADE, each .75 inches thick. The top edge includes a decorative molding. The total width of the door is 3.85 inches, and the overall height is 2.65 inches. The right side of the door is labeled "MDF CRISTAL - DURATEX".

VISTA 2: VISTA TRASEIRA

ESC.: 1 /

MDF RIVERA - DURATEX

MDF RIVERA - DURATEX

.37

3.85

MDF RIVERA - DURATEX

MDF RIVERA - DURATEX

.70

.70

.70

.70

MDF RIVERA - DURATEX

MDF CRISTAL - DURATEX

.70

.60 .70

3.85

MDF CRISTAL - DURATEX

VISTA 5 : VISTA LATERAL DIREITA

ESC*i*: 14

TURMA.:ARQUITETURA E URBANISMO

3 SEMESTRE

VISTC

FOLHA N°:

11

20

**ALUNOS: RAFAELA BEATRIZ RIBEIRO RODRIGUES
ANA LAURA OLIVEIRA TAQUES
VITORIA LORANA DA SILVA DOS SANTOS**


DISCIPLINA: PROJETO DE INTERIORES

R.A.: 177377-20
187322-20
168630-20

PROFESSORA: POLLYANA ROMAGNOLI TAMANIN


DATA: 23/04/2025

DETALHAMENTO

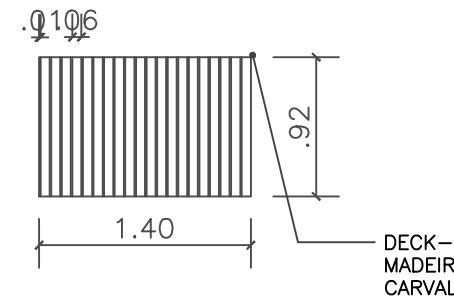


VISTA 1: VISTA SUPERIOR

ESC.: 1/50

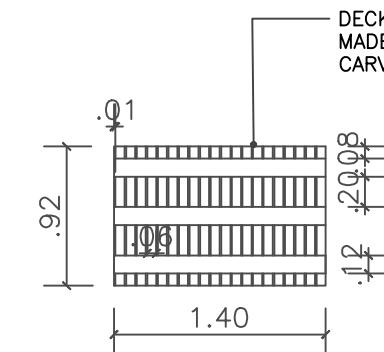


VISTA 2 : VISTA INFERIOR

ESC.: 1/50

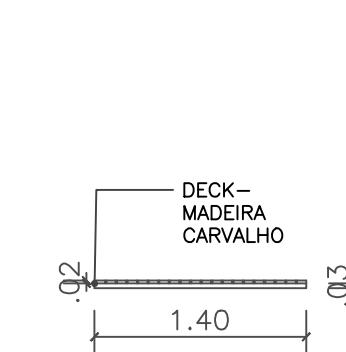

VISTA 3 : VISTA FRONTAL

ESC.: 1/50

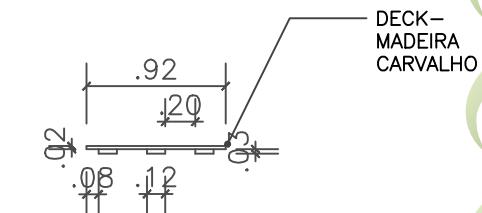


VISTA 4 : VISTA LATERAL

ESC.: 1/50

10


DETALHAMENTO DE MOBILIARIO - DECK

ESC.: 1/50

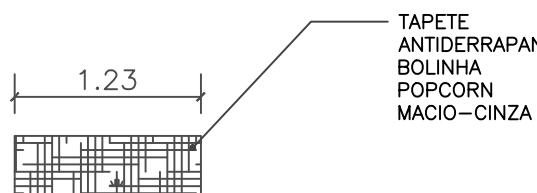

VISTA 1: VISTA SUPERIOR

ESC.: 1/50

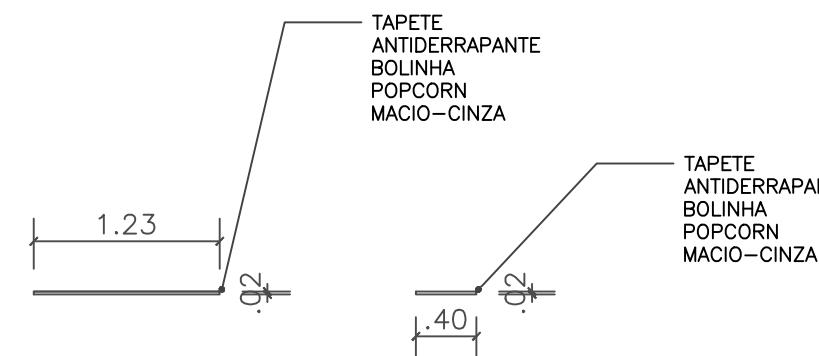

VISTA 2/3 : VISTA FRONTAL/LATERAL

ESC.: 1/50

11

DETALHAMENTO DE MOBILIARIO - TAPETE

ESC.: 1/50

ALUNOS: RAFAELA BEATRIZ RIBEIRO RODRIGUES
ANA LAURA OLIVEIRA TAQUES VITORIA
LORANA DA SILVA DOS SANTOS

DISCIPLINA: PROJETO DE INTERIORES I

R.A.: 177377-2024
187322-2024
168630-2024

PROFESSORA: POLLYANA ROMAGNOLI TAMANINI

TURMA: ARQUITETURA E URBANISMO
3 SEMESTRE

VISTO:


FOLHA N°:

13

DATA: 23/04/2025


20

DETALHAMENTO

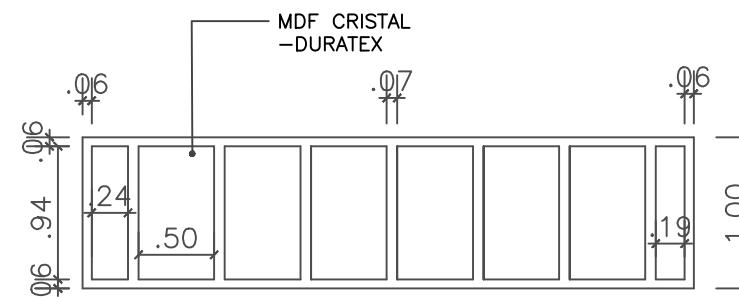

VISTA 1: VISTA FRONTAL

ESC.: 1/50

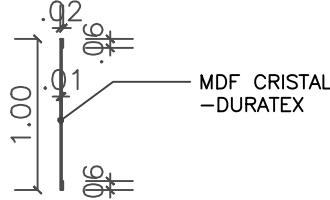

VISTA 2: VISTA LATERAL

ESC.: 1/50

DETALHAMENTO DE MOBILIARIO - PAINEL DE CABECEIRA

ESC.: 1/50

12
ALUNOS: RAFAELA
ANA
VITORIA

DISCIPLINA: PROJETO DE INTERIORES I

R.A.:

TURMA: ARQUITETURA E URBANISMO
3 SEMESTRE

VISTO:

FOLHA N°:

14

PROFESSORA: POLLYANA

DATA: 23/04/2025

20

MEMORIAL DESCRIPTIVO

QUARTO

	ITEM	QUANT.	INFORMAÇÕES
		1	CAMA DE CASAL VELEIRO - GRUPO BELLARTE
		3	NICHO 20X20 BRANCO MDF
		2	MESA DE CABECEIRA IRON 45 CM BRANCO E DOURADO

ALUNOS: RAFAELA BEATRIZ RIBEIRO RODRIGUES
ANA LAURA OLIVEIRA TAQUES
VITORIA LORANA DA SILVA DOS SANTOS

DISCIPLINA: PROJETO DE INTERIORES I

R.A.: 177377-2024
187322-2024
168630-2024

PROFESSORA: POLLYANA ROMAGNOLI TAMANINI


TURMA: ARQUITETURA E URBANISMO
3 SEMESTRE

VISTO:
DATA: 23/04/2025

FOLHA N°:
15
20

MEMORIAL DESCRIPTIVO

QUARTO

 ITEM	QUANT.	INFORMAÇÕES
	-	MDF BP VERDE JADE
	-	MDF CRISTAL - DURATEX
	-	MDF RIVERA - DURATEX
	1	ESPELHO AFRODITE LUMINA ELEGANCE - DUBLIM DESIGN, TAMANHO M

ALUNOS: RAFAELA BEATRIZ RIBEIRO RODRIGUES
ANA LAURA OLIVEIRA TAQUES
VITORIA LORANA DA SILVA DOS SANTOS

R.A.: 177377-2024
187322-2024
168630-2024

TURMA: ARQUITETURA E URBANISMO
3 SEMESTRE

VISTO:

FOLHA N°:

16

DISCIPLINA: PROJETO DE INTERIORES I

PROFESSORA: POLLYANA ROMAGNOLI TAMANINI

DATA: 23/04/2025

20

MEMORIAL DESCRIPTIVO

QUARTO

ITEM	QUANT.	INFORMAÇÕES
	1	LUSTRE GRAPP HORIZONTAL 12 GOLDEN ART
	2	ARANDELA LED ZANA - NORDECOR

ALUNOS: RAFAELA BEATRIZ RIBEIRO RODRIGUES
ANA LAURA OLIVEIRA TAQUES
VITORIA LORANA DA SILVA DOS SANTOS

DISCIPLINA: PROJETO DE INTERIORES I

R.A.: 177377-2024
187322-2024
168630-2024

PROFESSORA: POLLYANA ROMAGNOLI TAMANINI

TURMA: ARQUITETURA E URBANISMO
3 SEMESTRE

VISTO:
DATA: 23/04/2025

FOLHA N°:
17
20

MEMORIAL DESCRIPTIVO

BANHEIRO

ITEM	DESCRITIVO QUANT.	INFORMAÇÕES
	1	BANHEIRA CARMÉLIA - AQUALAX
	1	VASO SANITÁRIO CAIXA
	2	CUBA DE APOIO ESQUADRO 40 - SABBIA
	2	ESPELHO AFRODITE LUMINA ELEGANCE - DUBLIM DESIGN, TAMANHO M

ALUNOS: RAFAELA BEATRIZ RIBEIRO RODRIGUES
ANA LAURA OLIVEIRA TAQUES
VITORIA LORANA DA SILVA DOS SANTOS

DISCIPLINA: PROJETO DE INTERIORES I

R.A.: 177377-2024
187322-2024
168630-2024

PROFESSORA: POLLYANA ROMAGNOLI TAMANINI


TURMA: ARQUITETURA E URBANISMO
3 SEMESTRE

VISTO:
DATA: 23/04/2025

FOLHA N°:
18
20

MEMORIAL DESCRIPTIVO

BANHEIRO

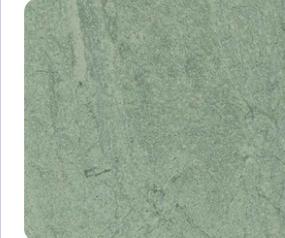ITEM	QUANT.	INFORMAÇÕES
	2	TORNEIRA DE MESA PARA LAVATÓRIO PURIST KOHLER
	-	REVESTIMENTO QUARTZO SUPER BRANCO PARA A BANCADA DO BANHEIRO
		PORCELANATO PACIFIQUE CGN HARD SMALTADO BOLD PORTINARI-REVESTI
	1	TAPETE DE BANHO DE PEDRA ABSORVENTE COR CINZA 40X60 CM

ALUNOS: RAFAELA BEATRIZ RIBEIRO RODRIGUES
ANA LAURA OLIVEIRA TAQUES
VITORIA LORANA DA SILVA DOS SANTOS

R.A.: 177377-2024
187322-2024
168630-2024

TURMA: ARQUITETURA E URBANISMO
3 SEMESTRE

VISTO:

FOLHA N°:

19

DISCIPLINA: PROJETO DE INTERIORES I


PROFESSORA: POLLYANA ROMAGNOLI TAMANINI

DATA: 23/04/2025

20

MEMORIAL DESCRIPTIVO

VARANDA

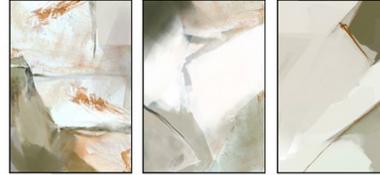ITEM	QUANT.	INFORMAÇÕES
	1	SOFÁ TRANCOSO TIDELLI
	3	ARANDELA LED ZANA - NORDECOR
	1	KIT 2 MESA DE CENTRO MADEIRA DESIGN ORGÂNICO 69/77 CM - MEL
	1	QUADRO TRÍPTICO SETTLED 04+05 + CANDURAS DO DESERTO 05 - ART TONIAL

ALUNOS: RAFAELA
ANA
VITORIA

DISCIPLINA: PROJETO DE INTERIORES I

R.A.:

TURMA: ARQUITETURA E URBANISMO
3 SEMESTRE

VISTO:

FOLHA N°:

20

PROFESSORA: POLLYANA

DATA: 23/04/2025

20